



nike event spatial design

deck 003 10.07.2026

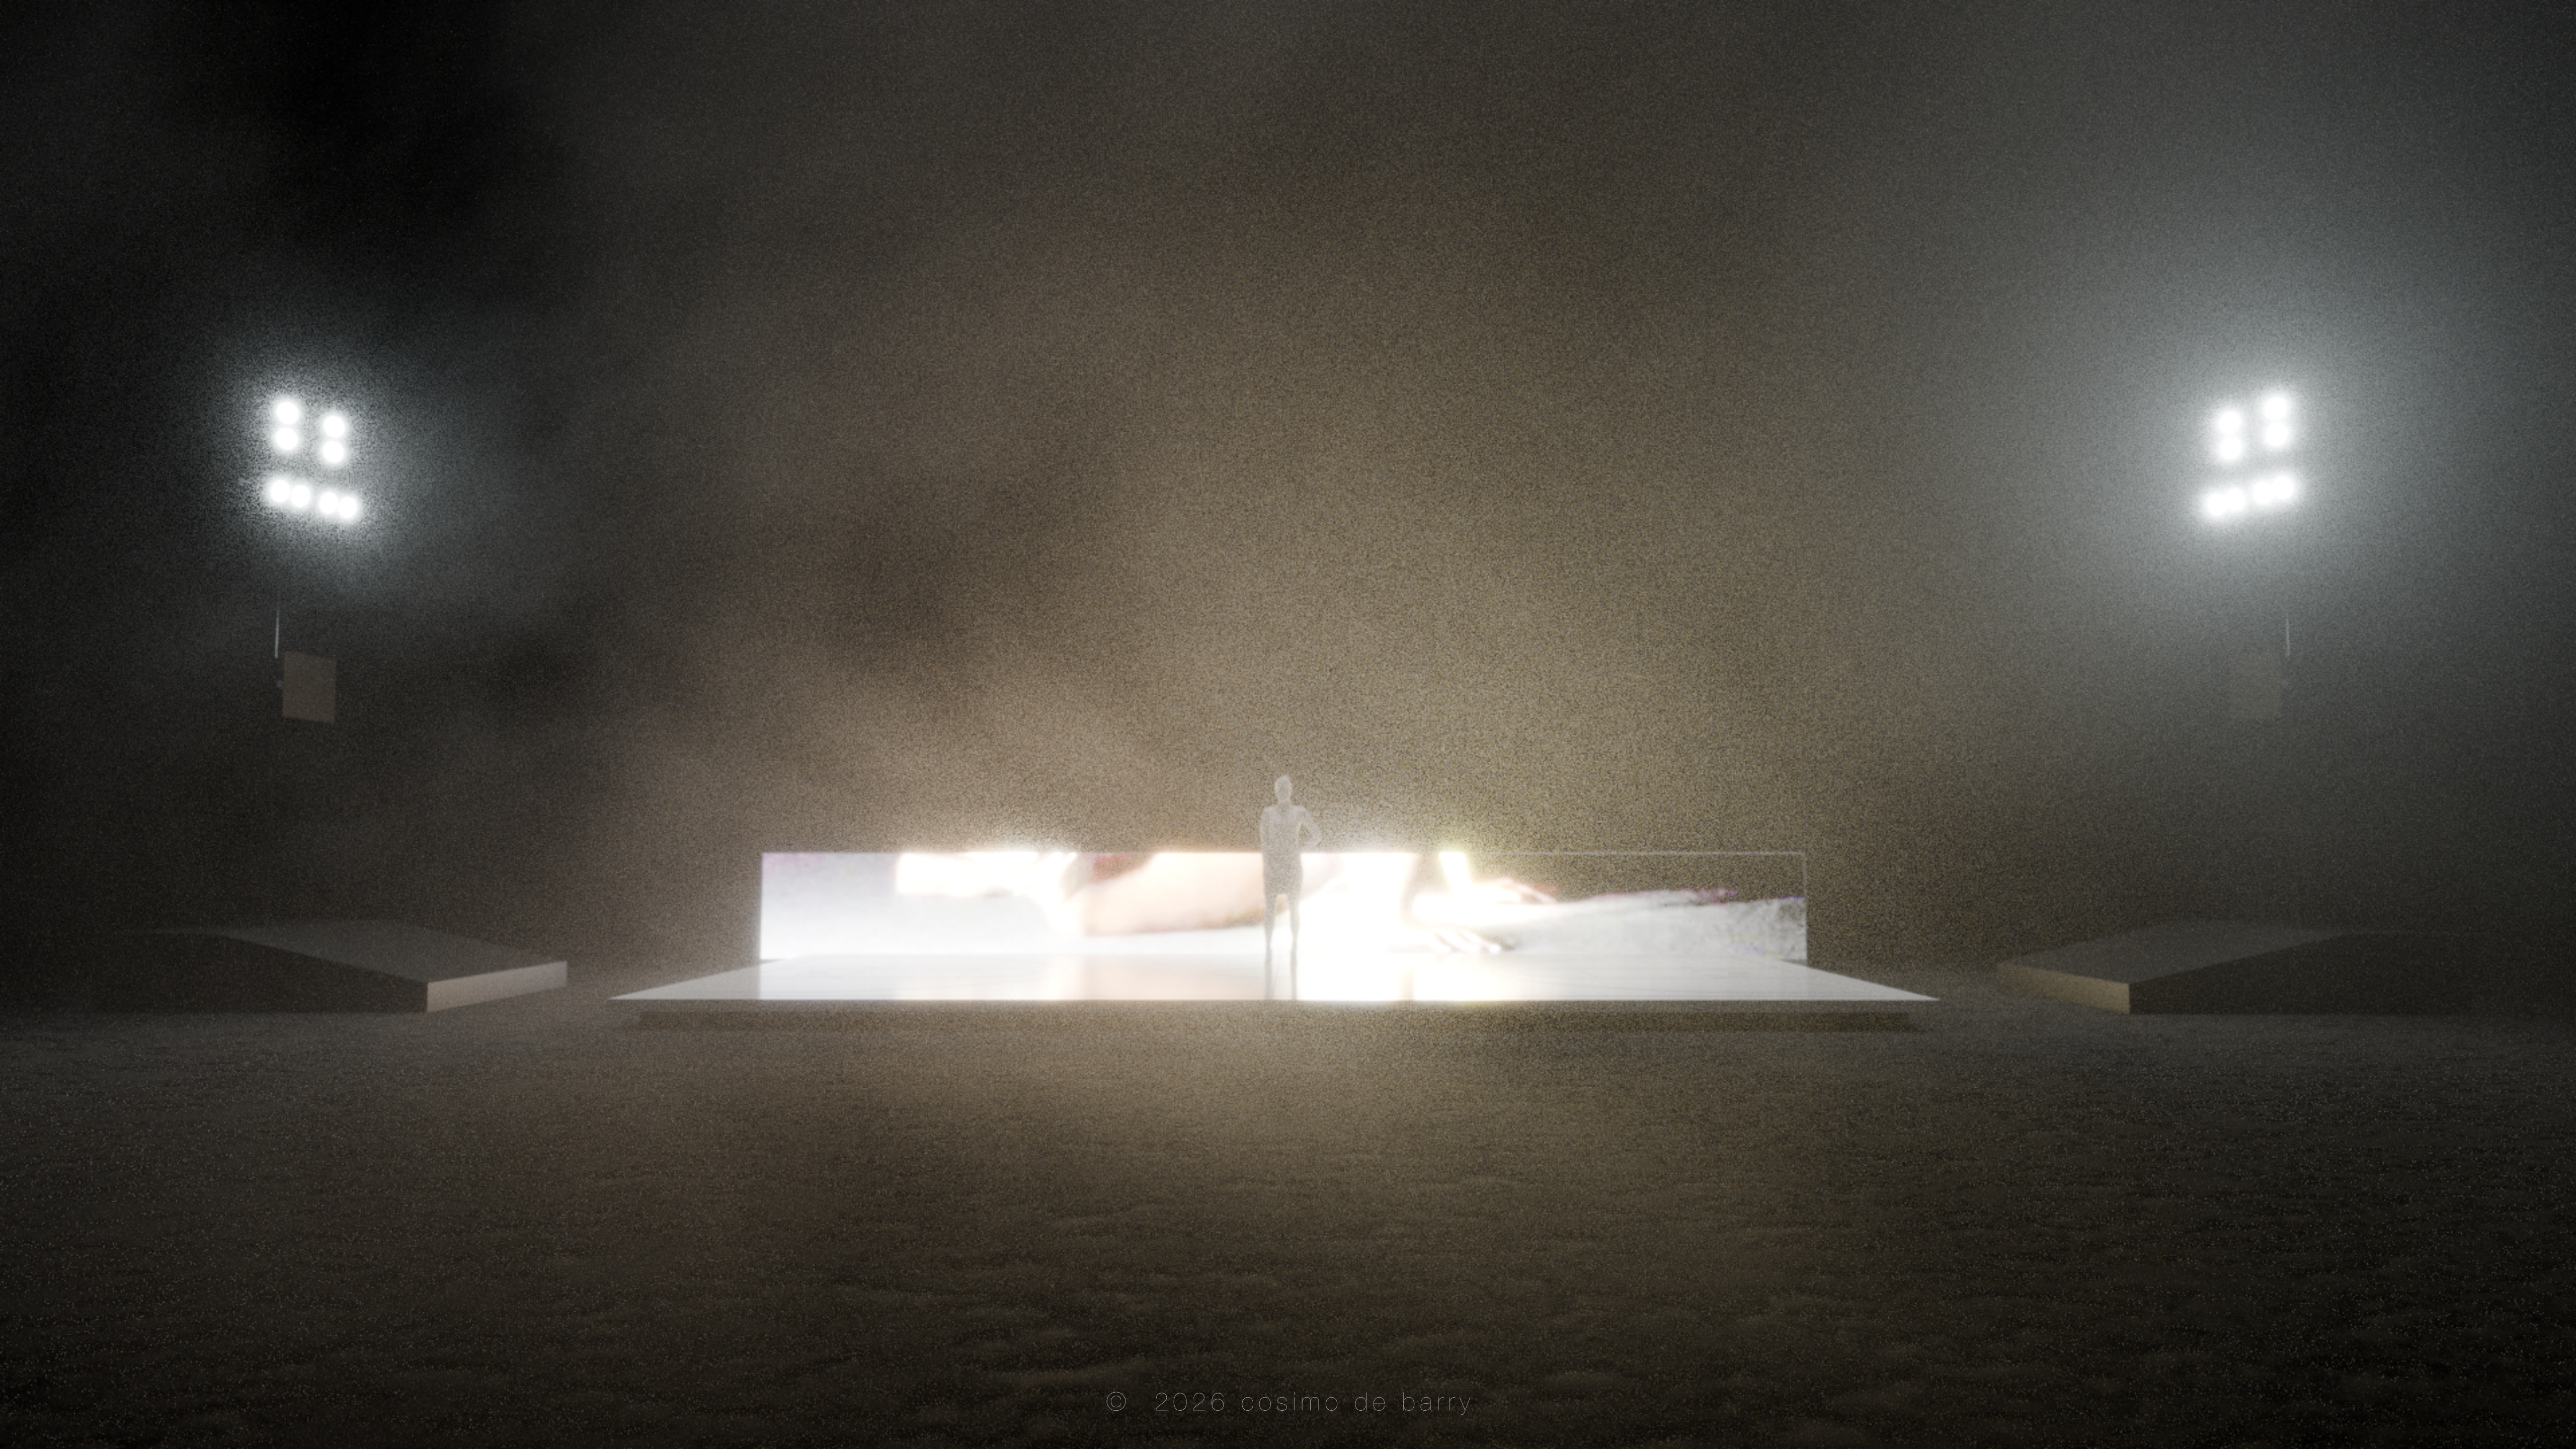

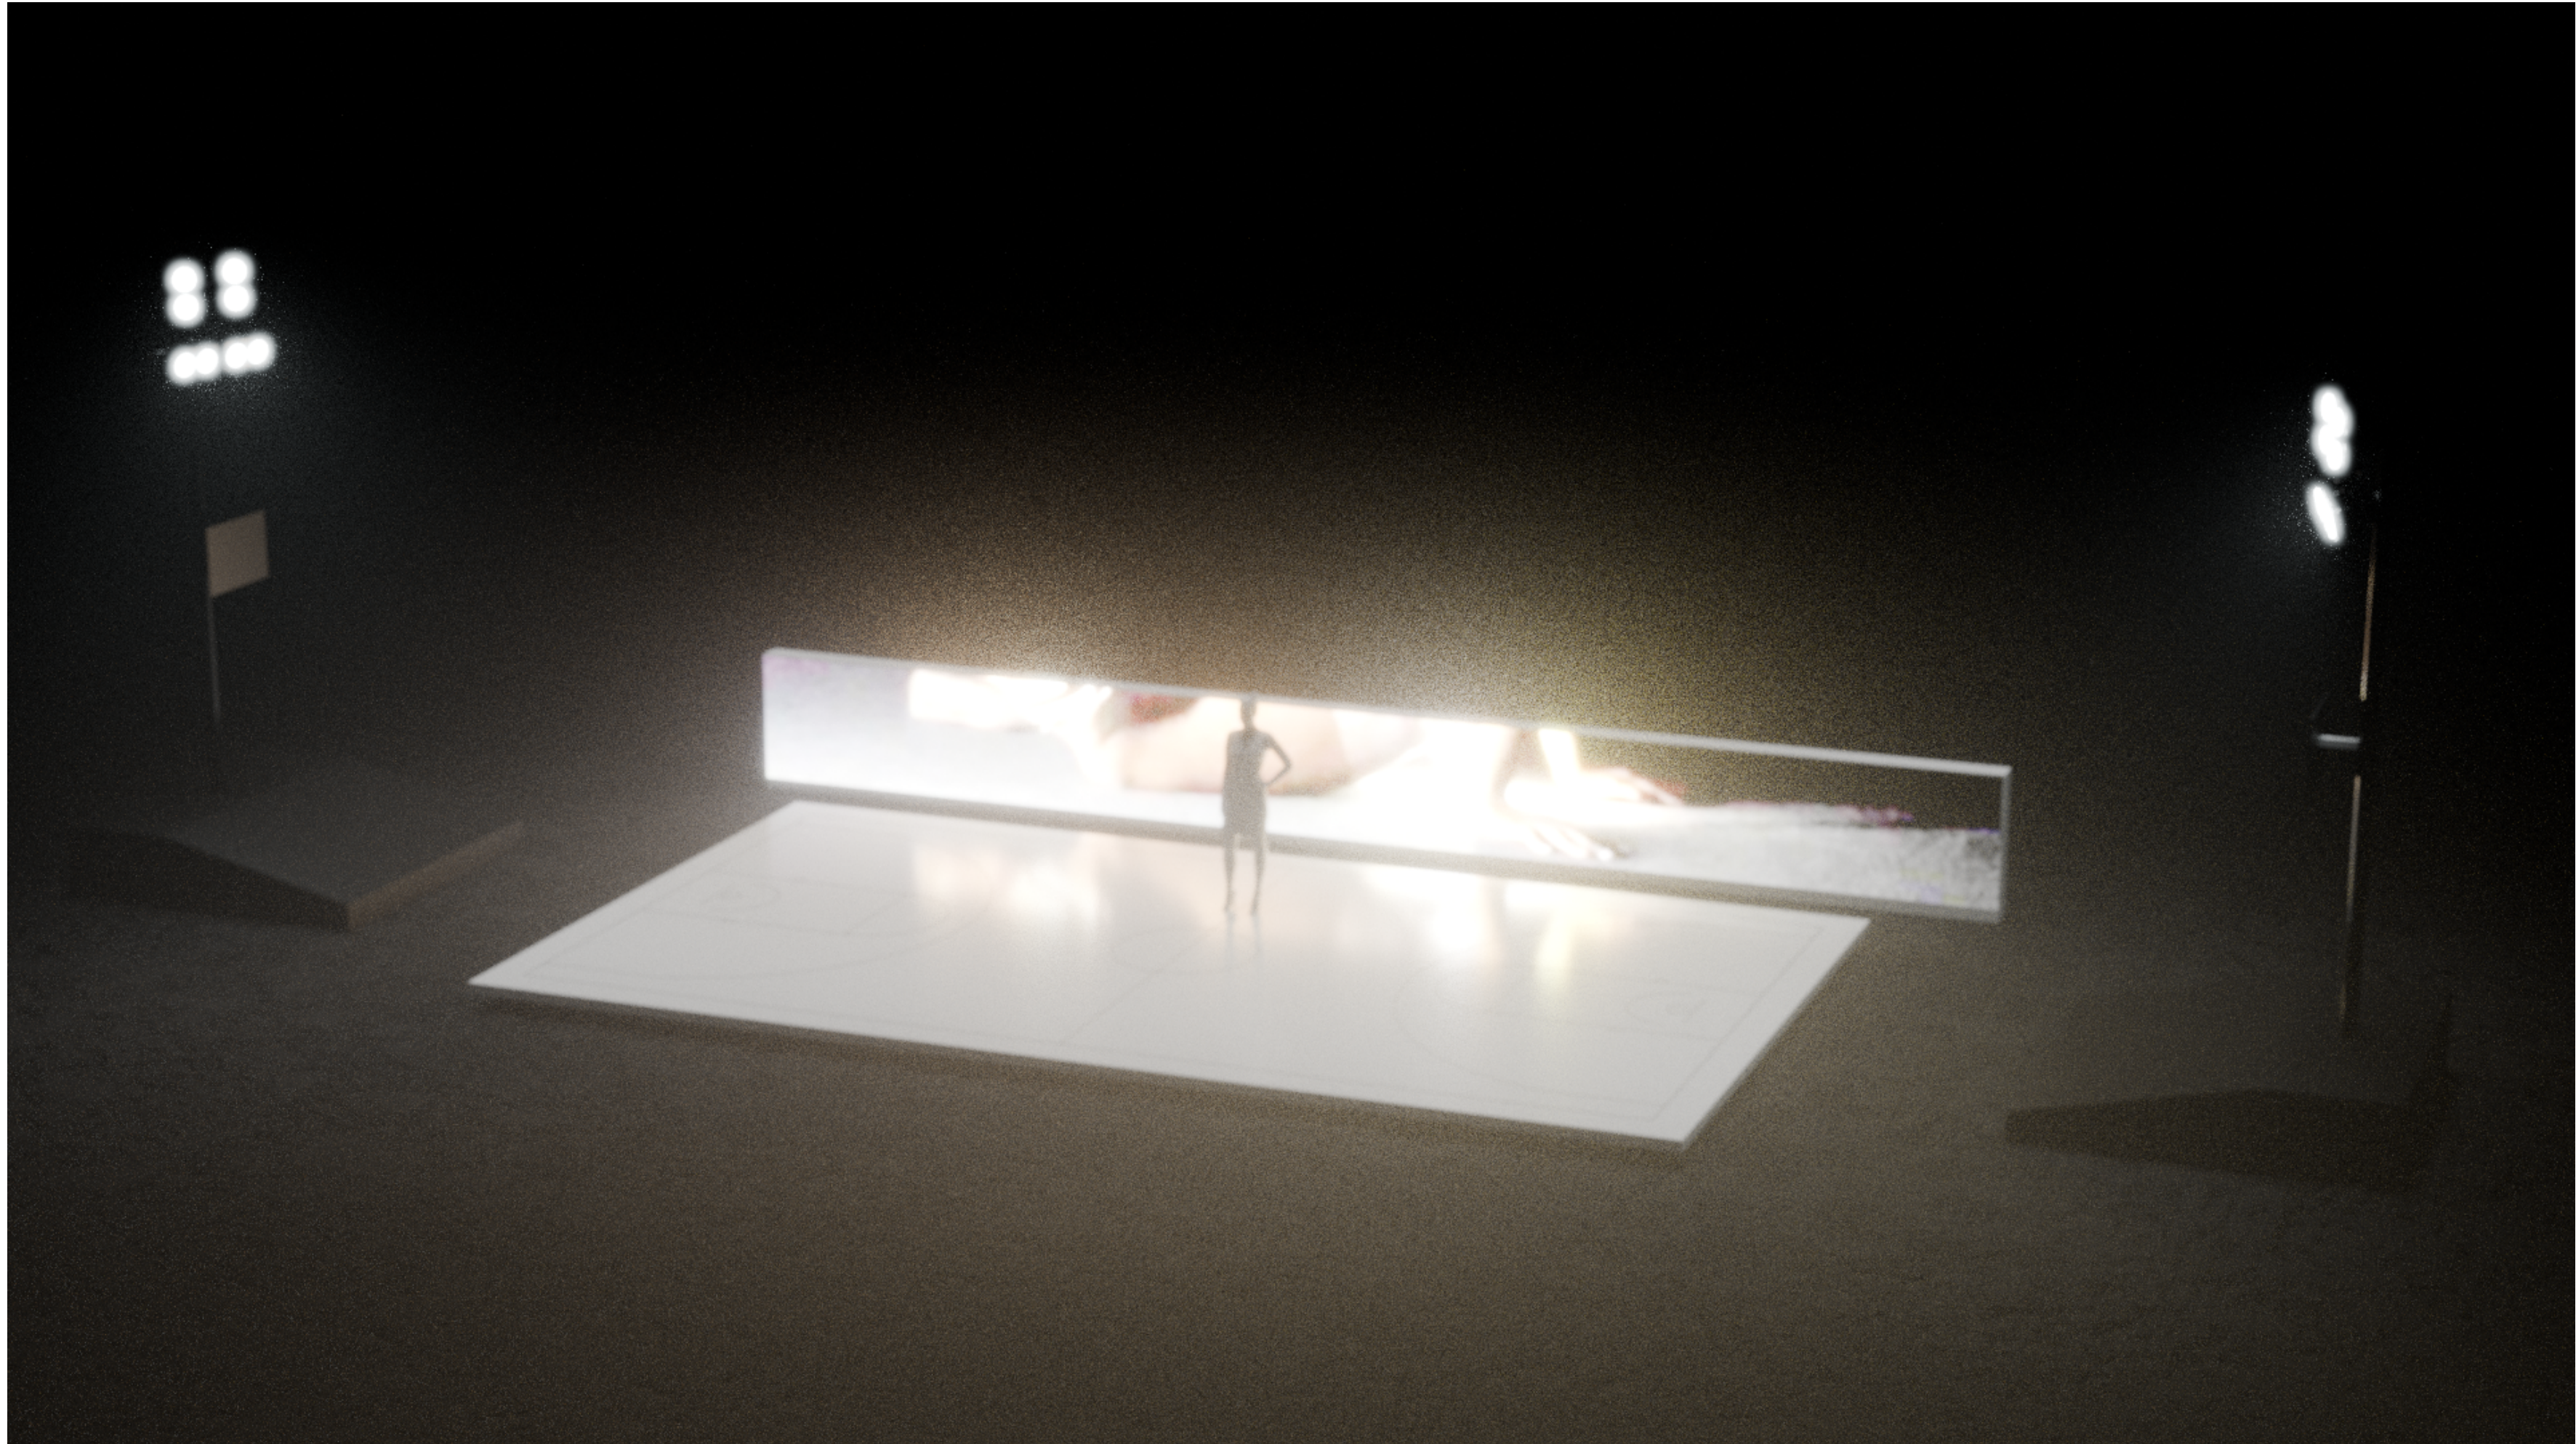






Concept Recap

The initial concept deck proposed a super light, white, and clean aesthetic, with the aim of creating a striking, unique, and ownable visual identity for this Nike event.


The initial mono-material approach has been developed. All objects share a high gloss finish, however the platform now acts as the singular white surface.

Key Elements

1. WHITE GLOSS STAGE
2. 10M LED PERIMETER SCREEN
3. BLACK GLOSS DAYBEDS + LIGHTING MAST
4. KISS CAM
5. BLEACHER (OUT OF BUDGET)

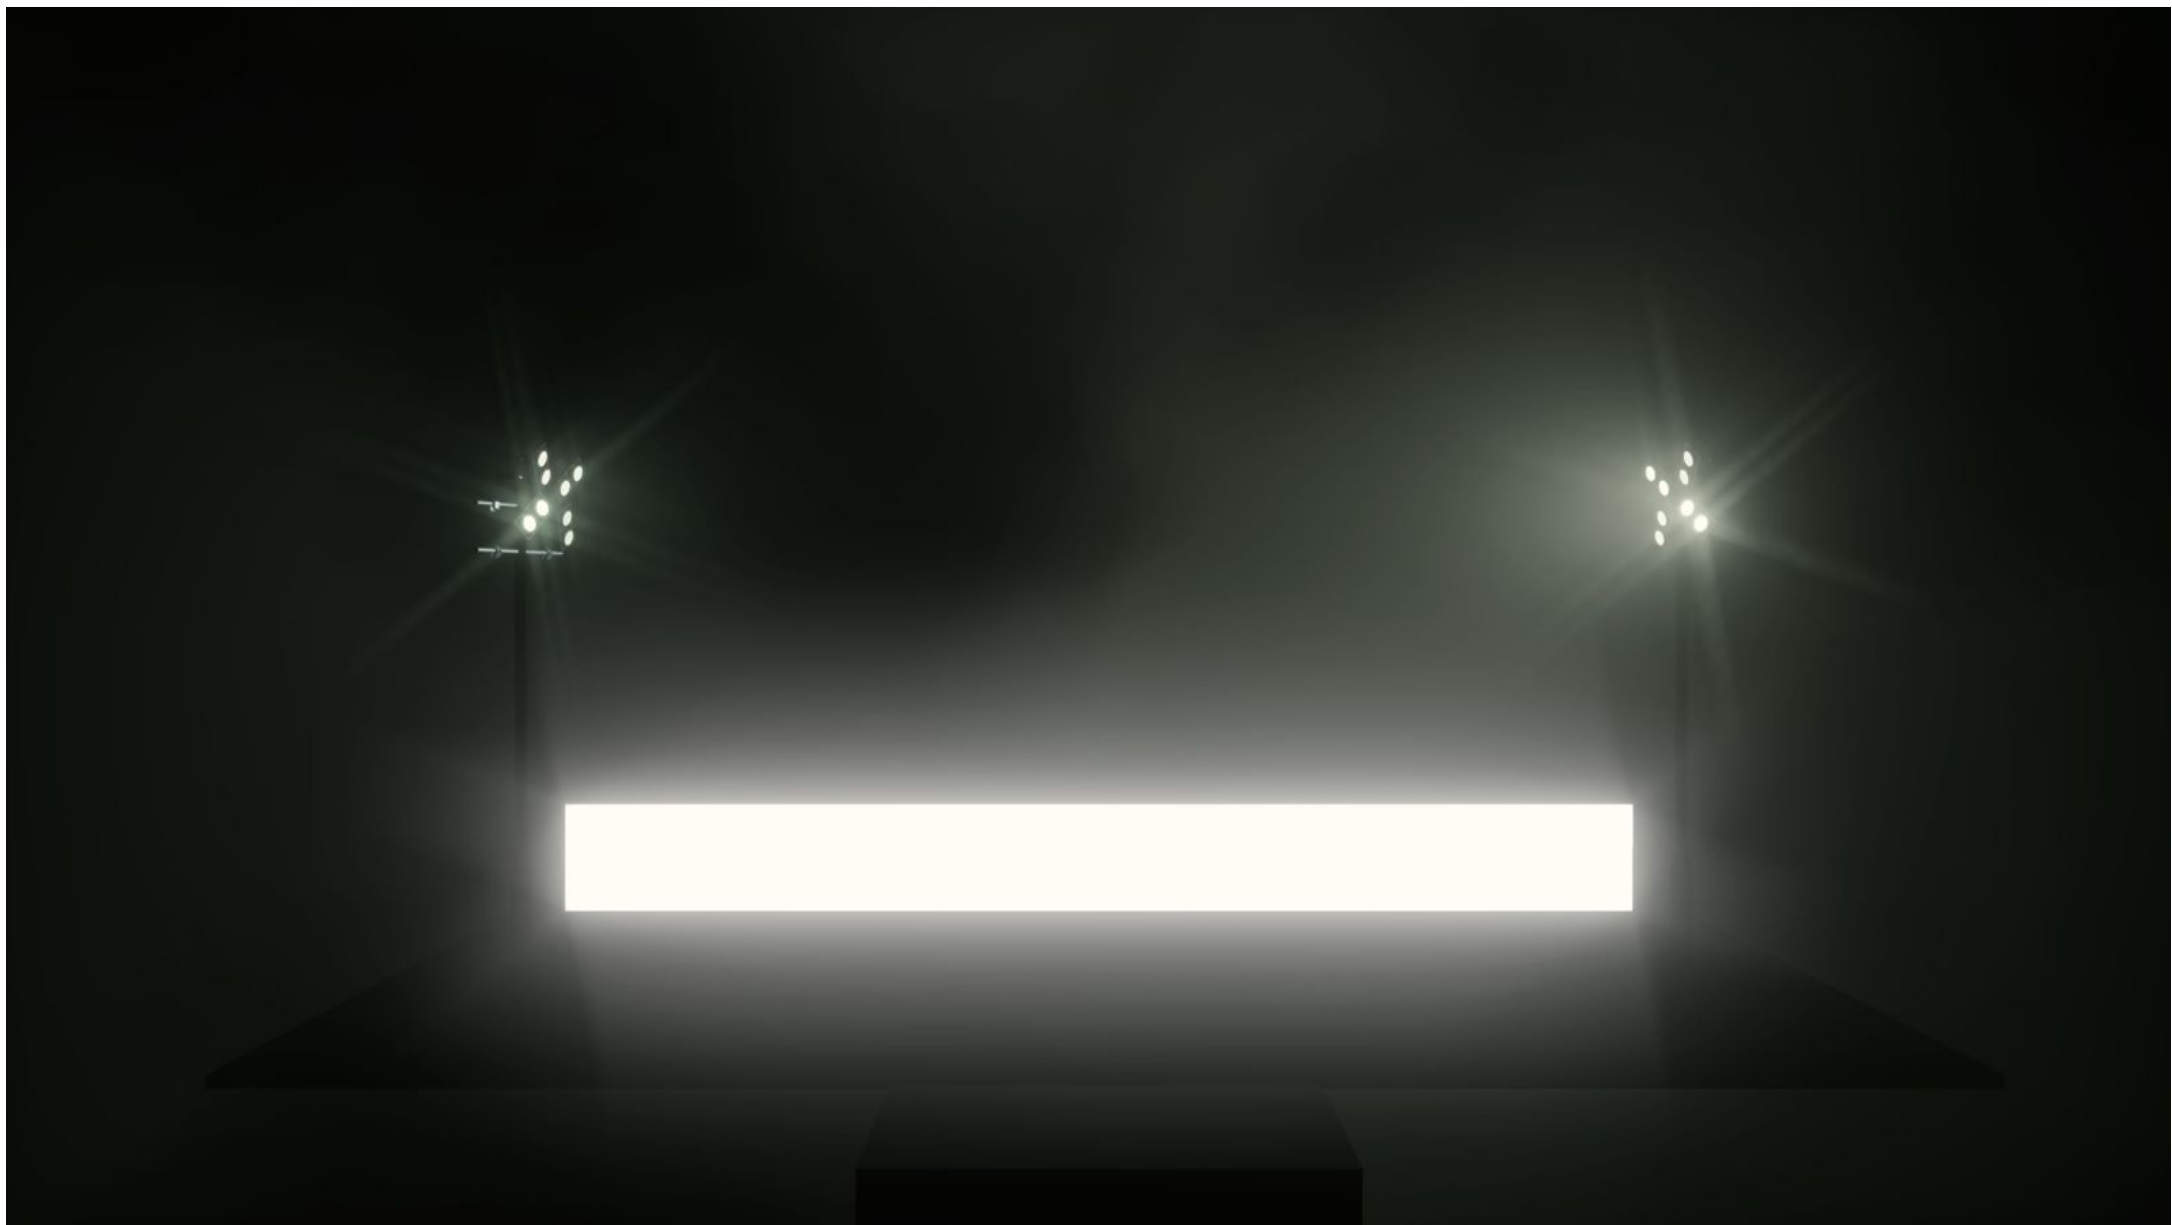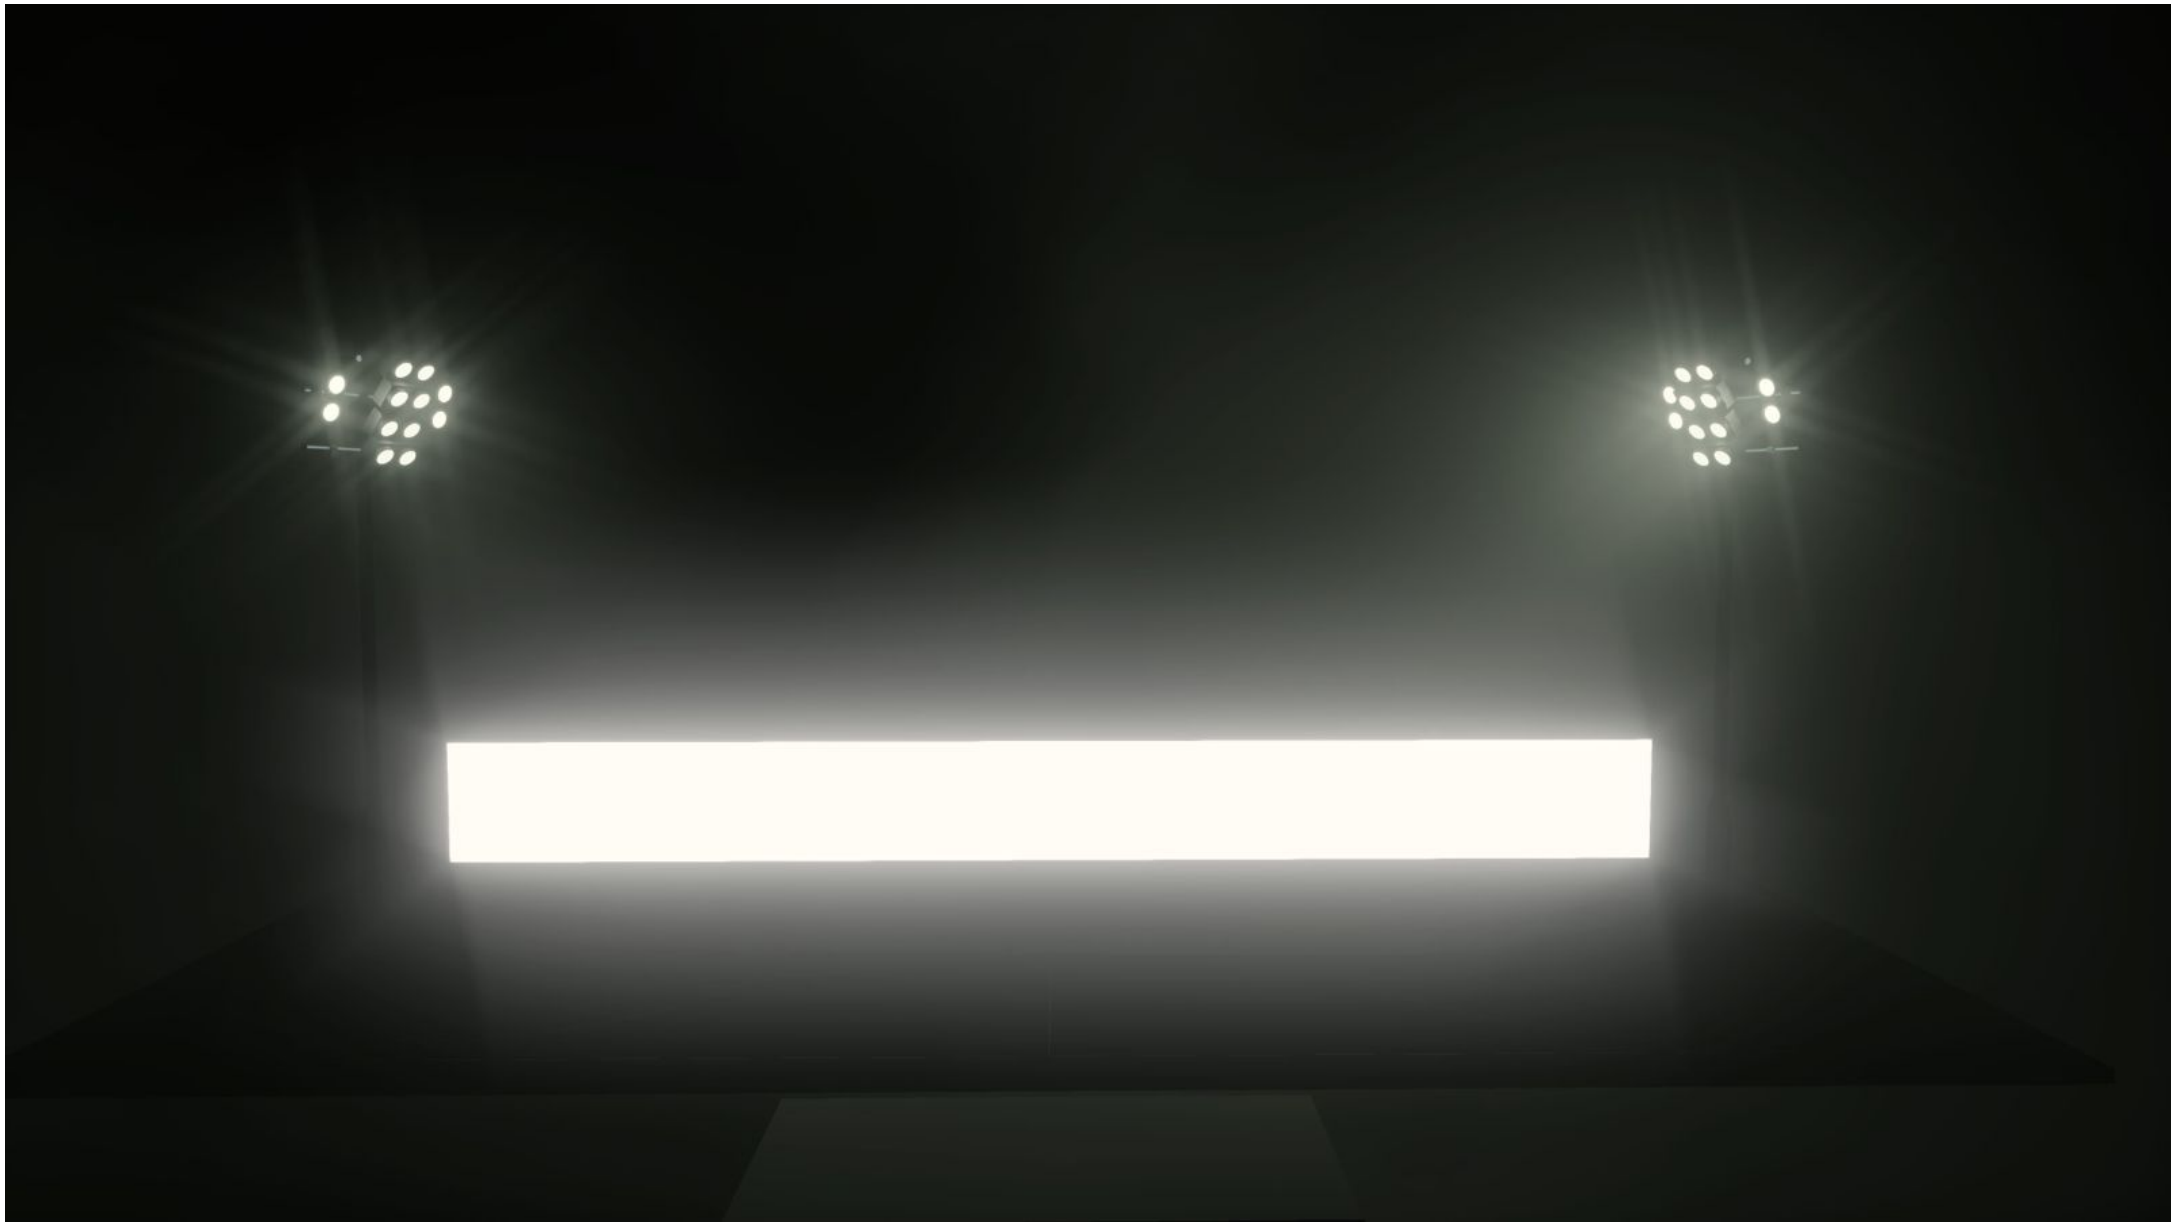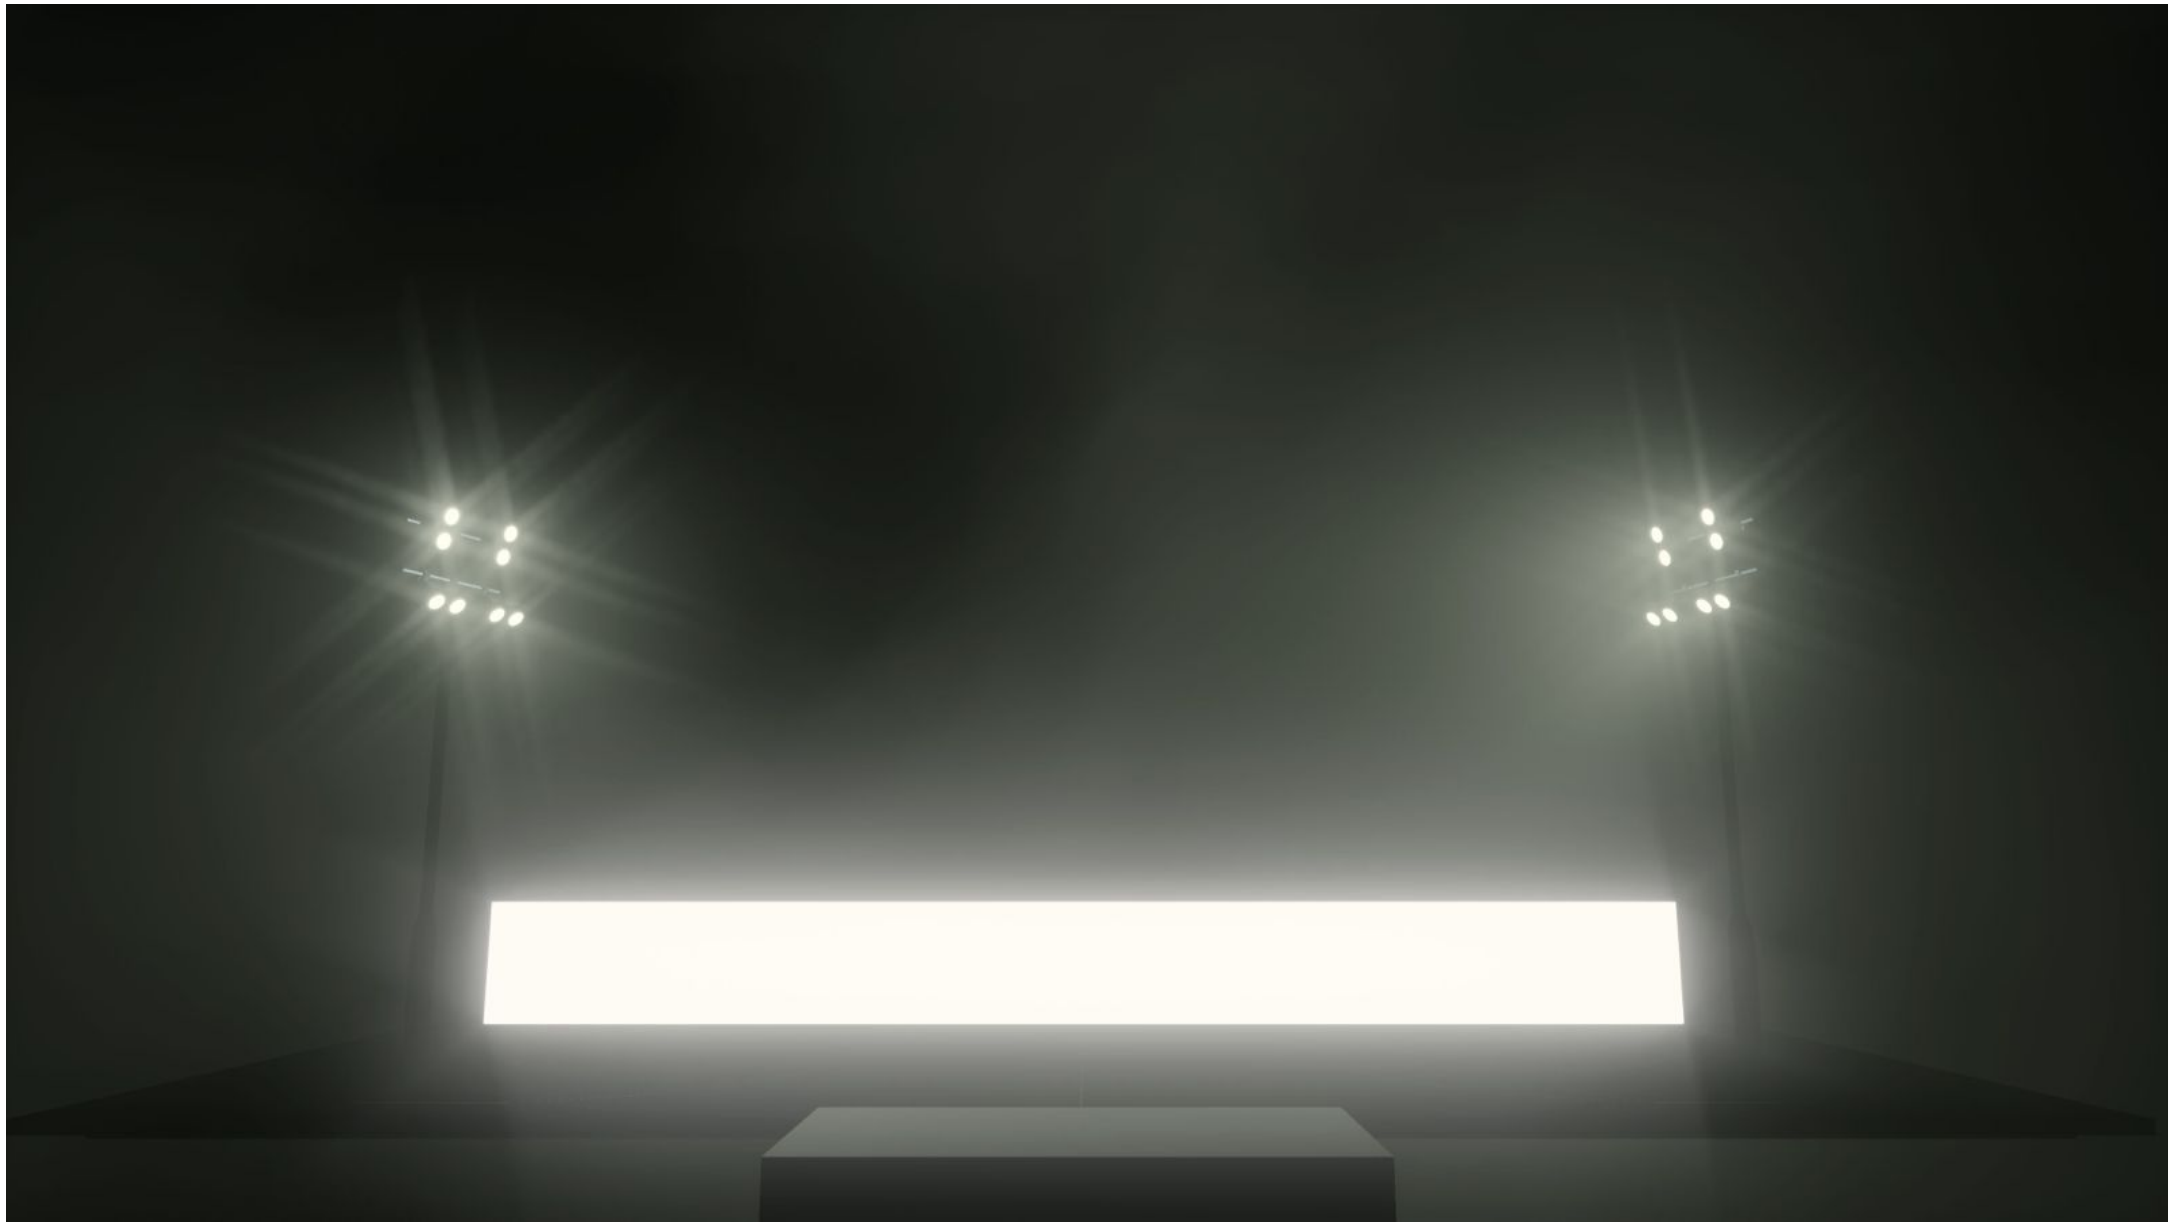


Lighting Options
These renders provide a more realistic visualisation of what lighting will look like. The three images correspond to three different arrangements we are currently exploring.

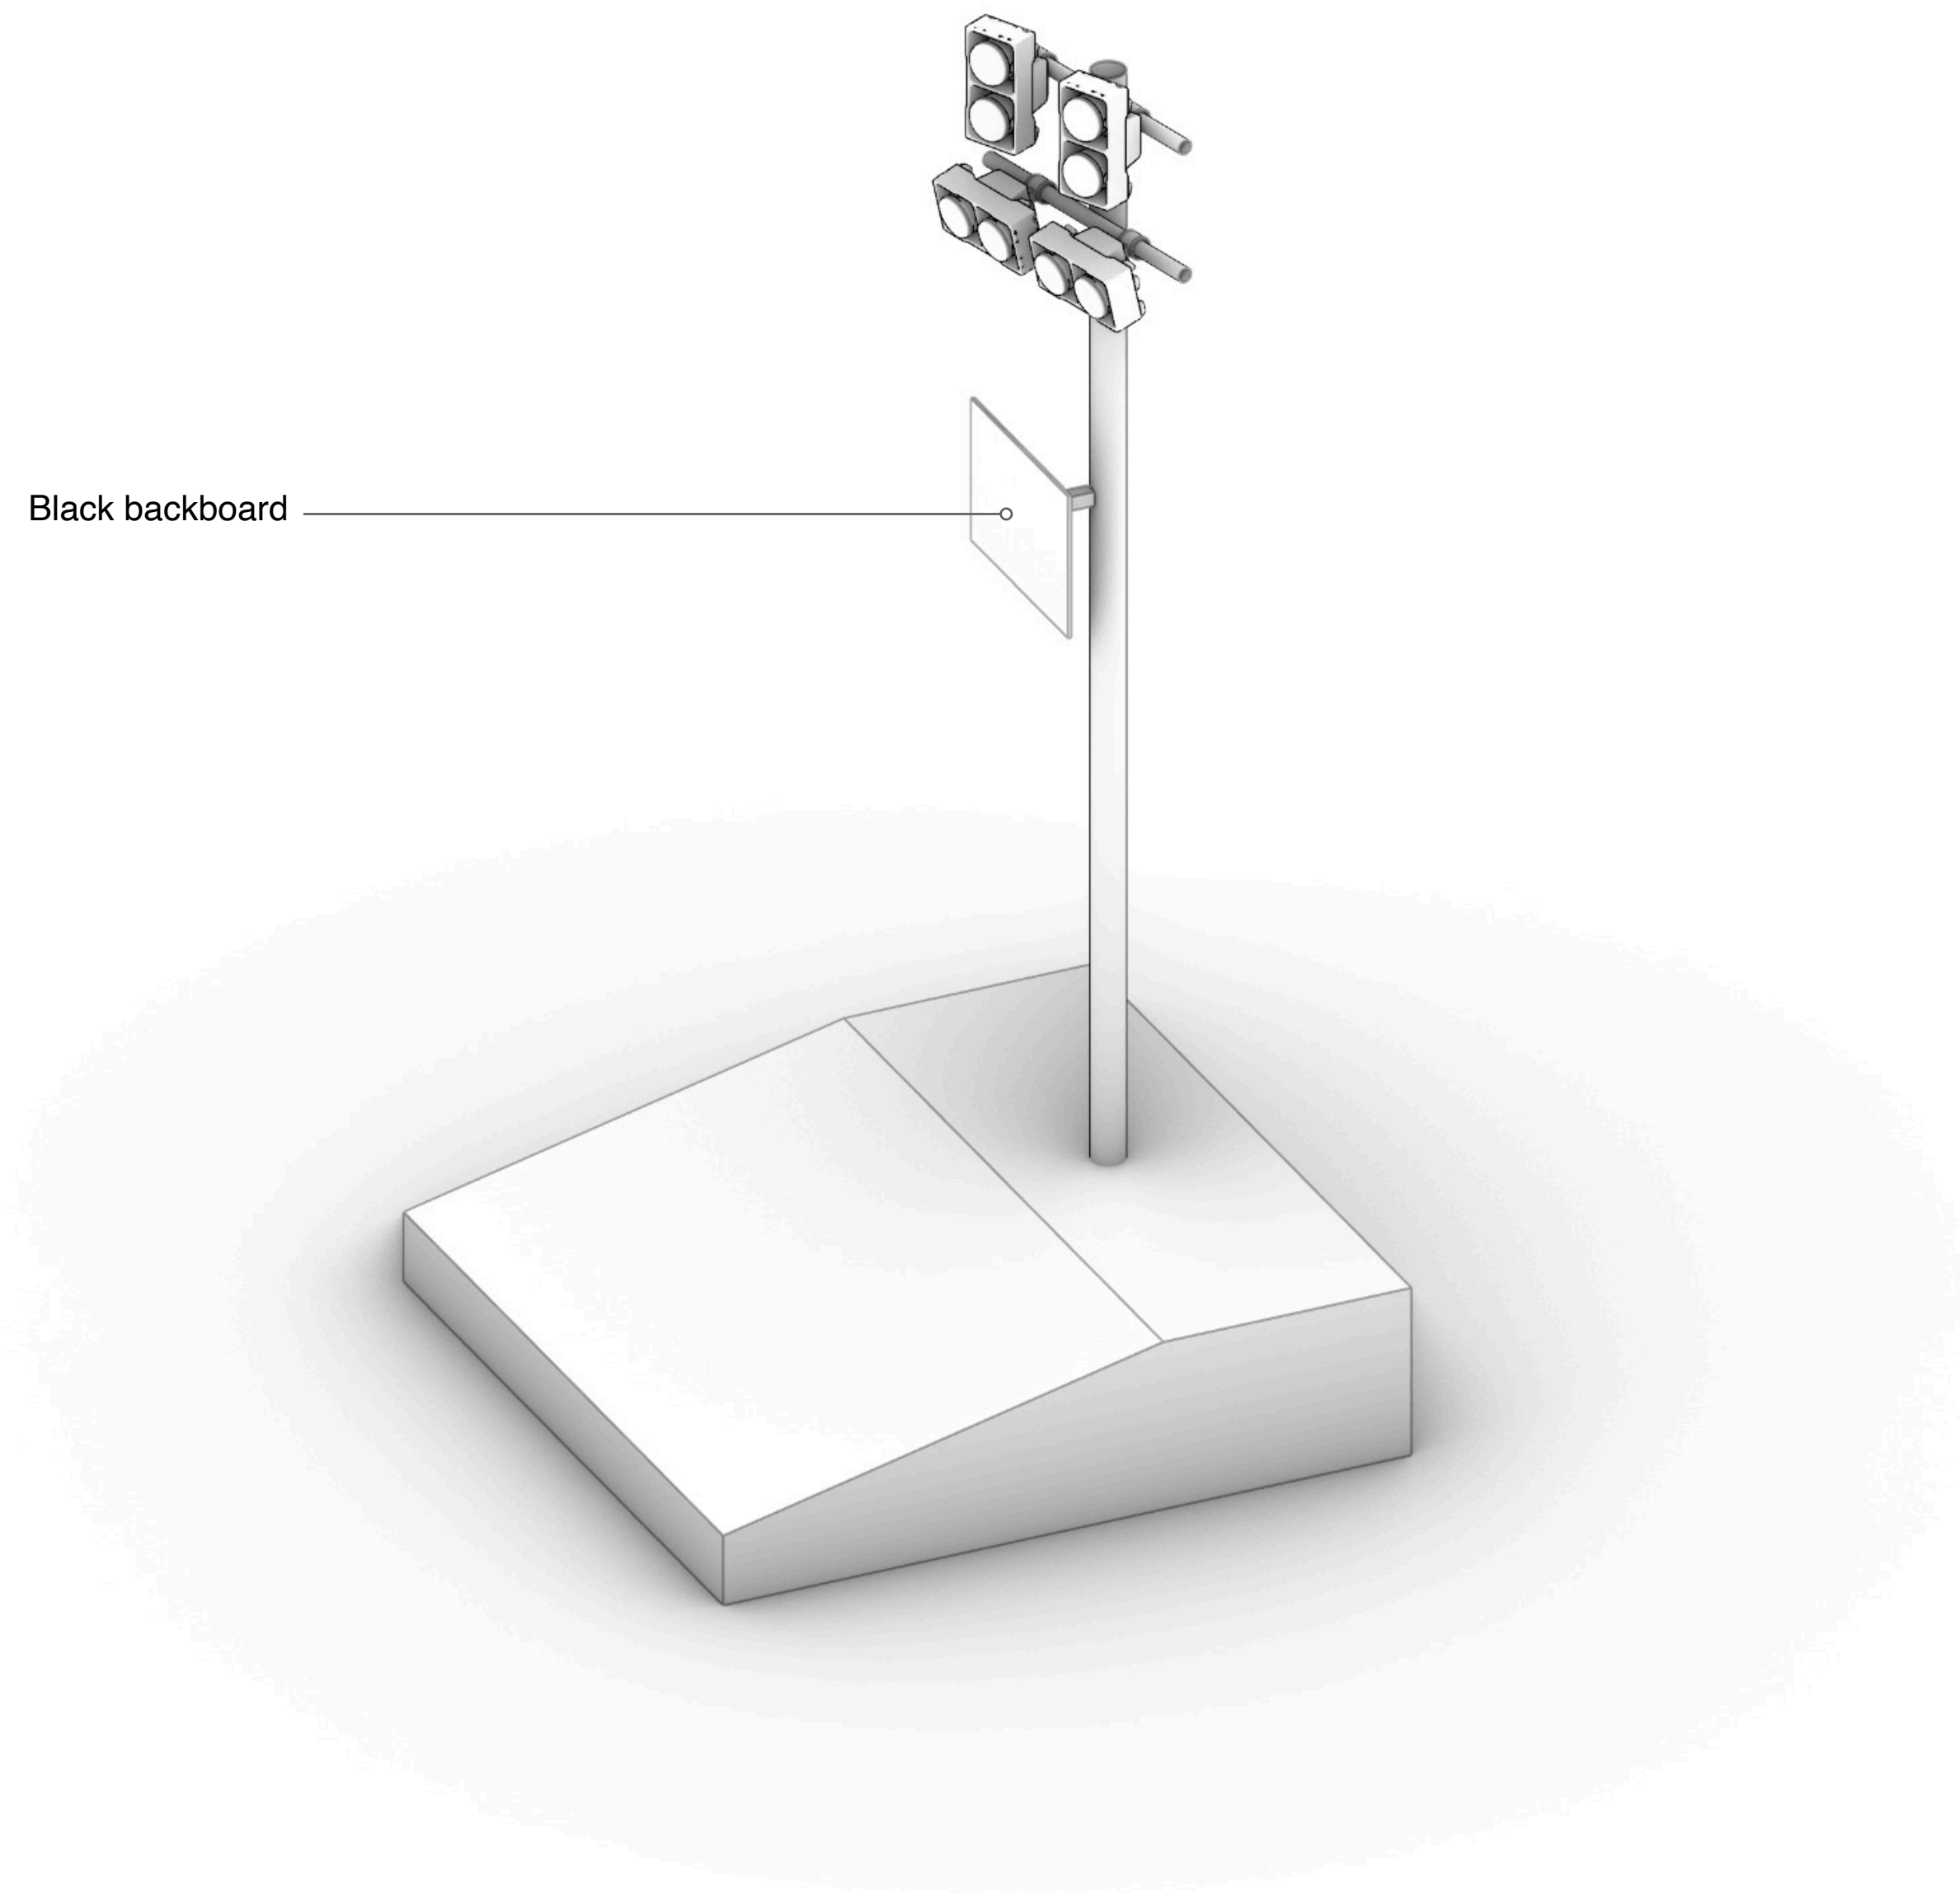


Base + Lighting Mast


The basket ball hoop has been converted into a rig for lighting and integrated with a base. The base has the potential to acts as a daybed as well as a performance platform. The slope was introduced to be reminiscent of a bleacher.

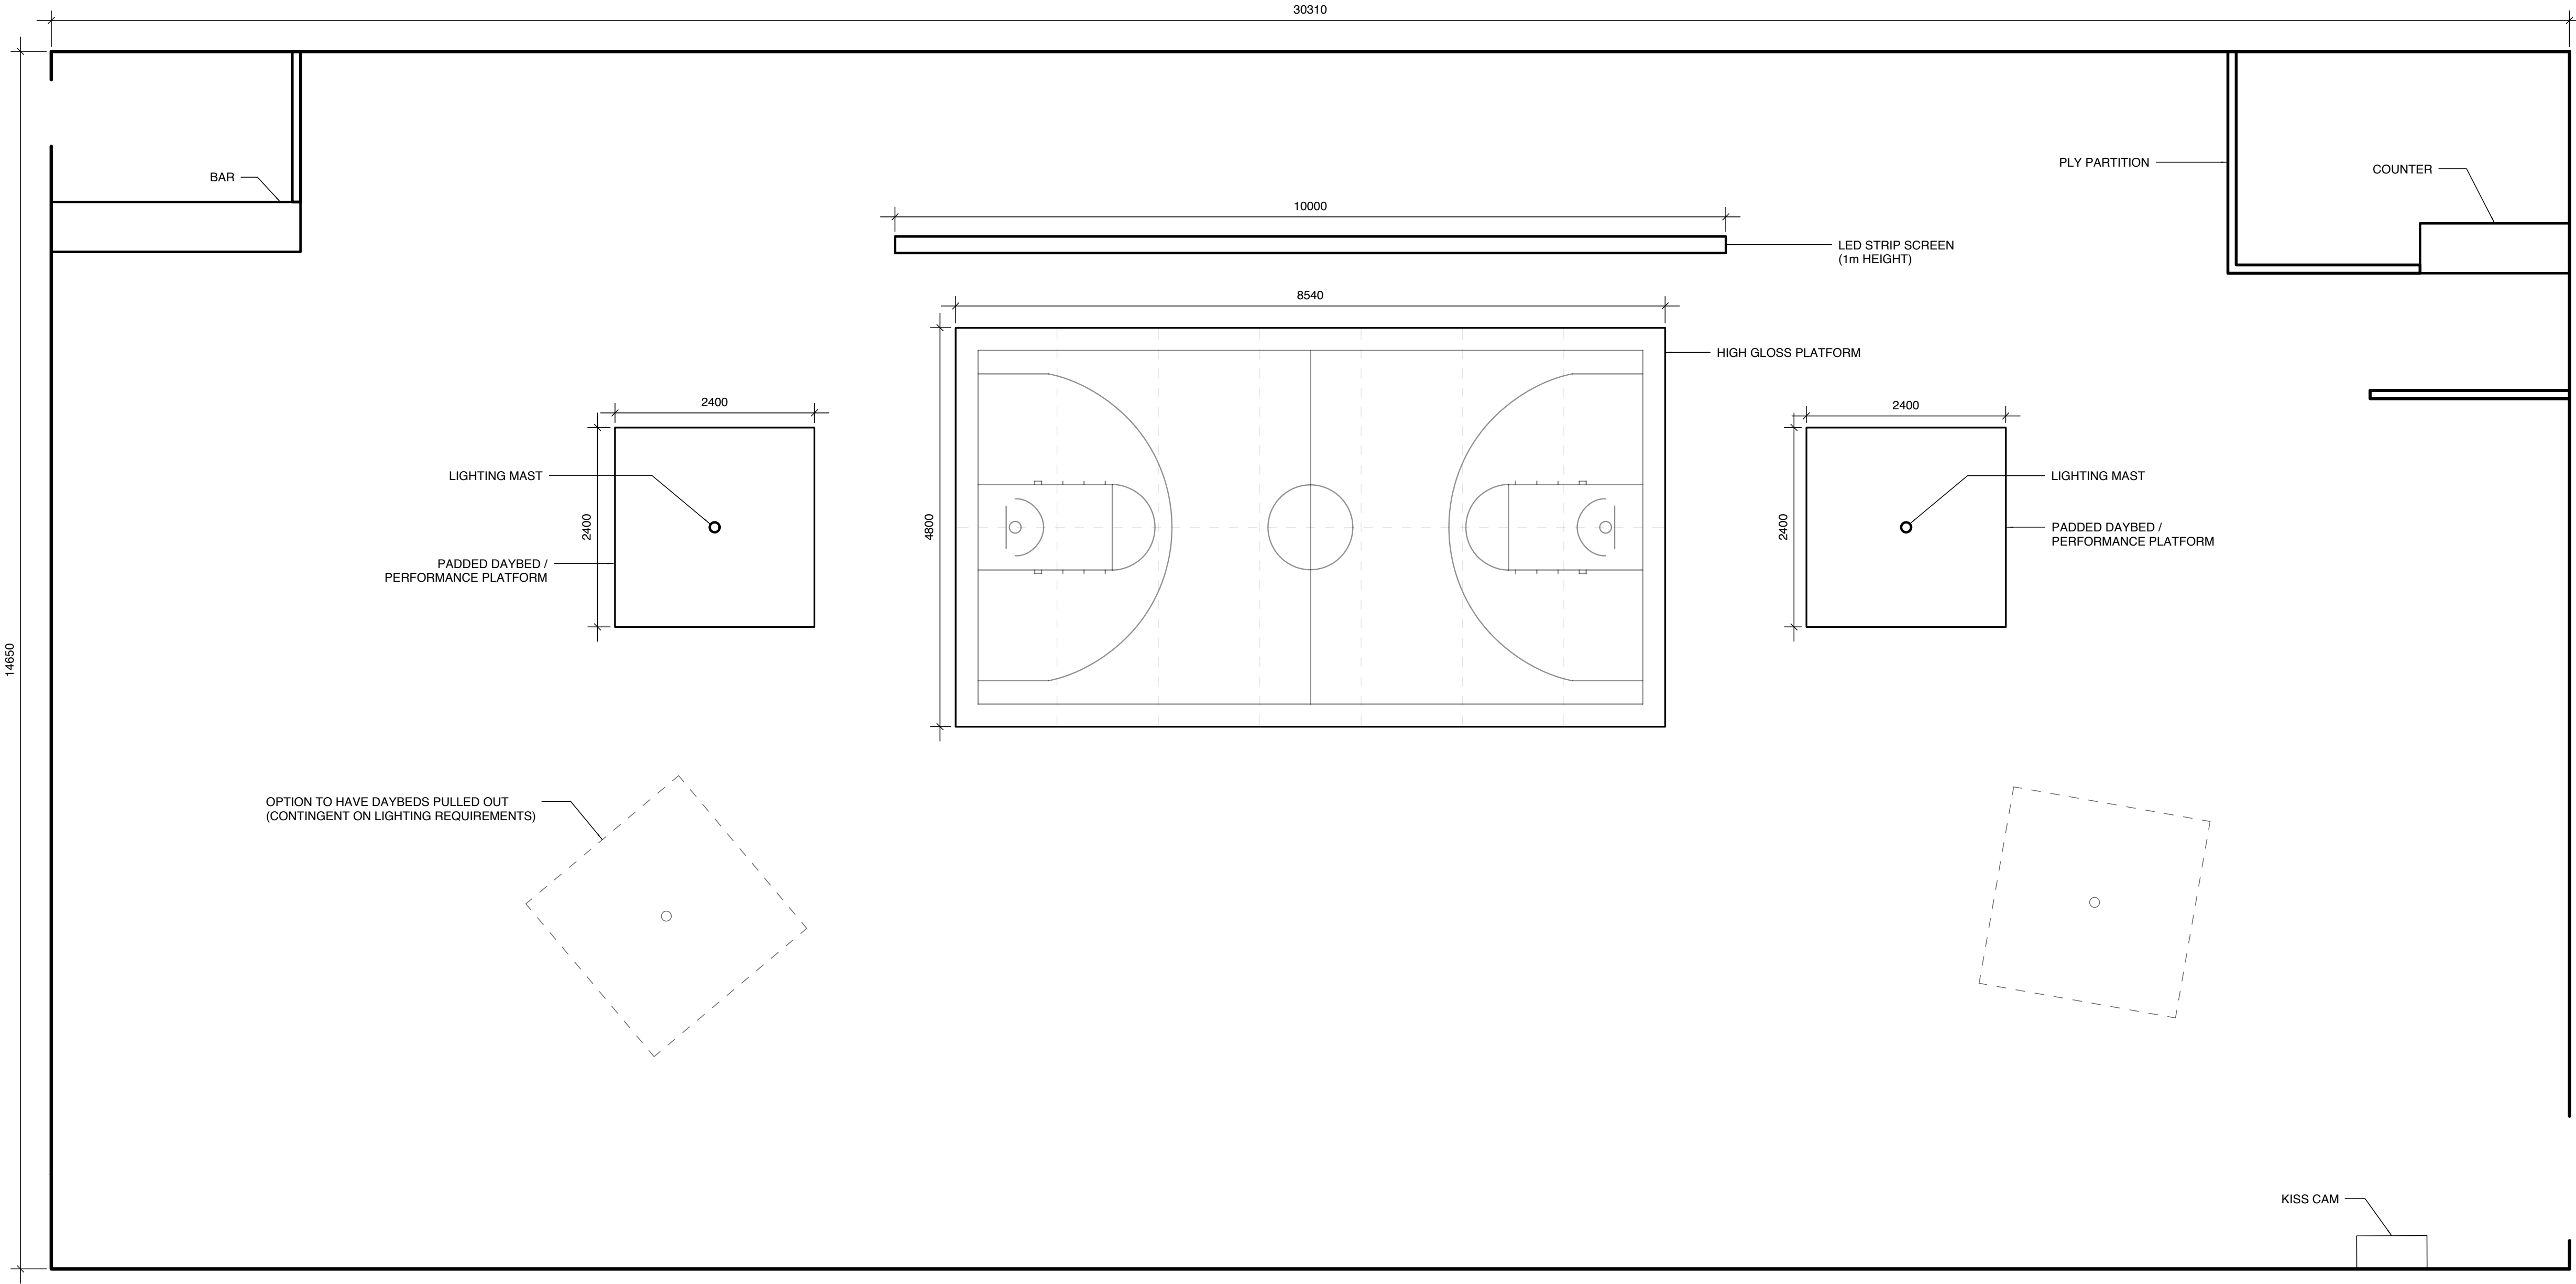

Plan: Dimensions & Objects
Room dimensions are indicative and based on the Bermondsey venue.

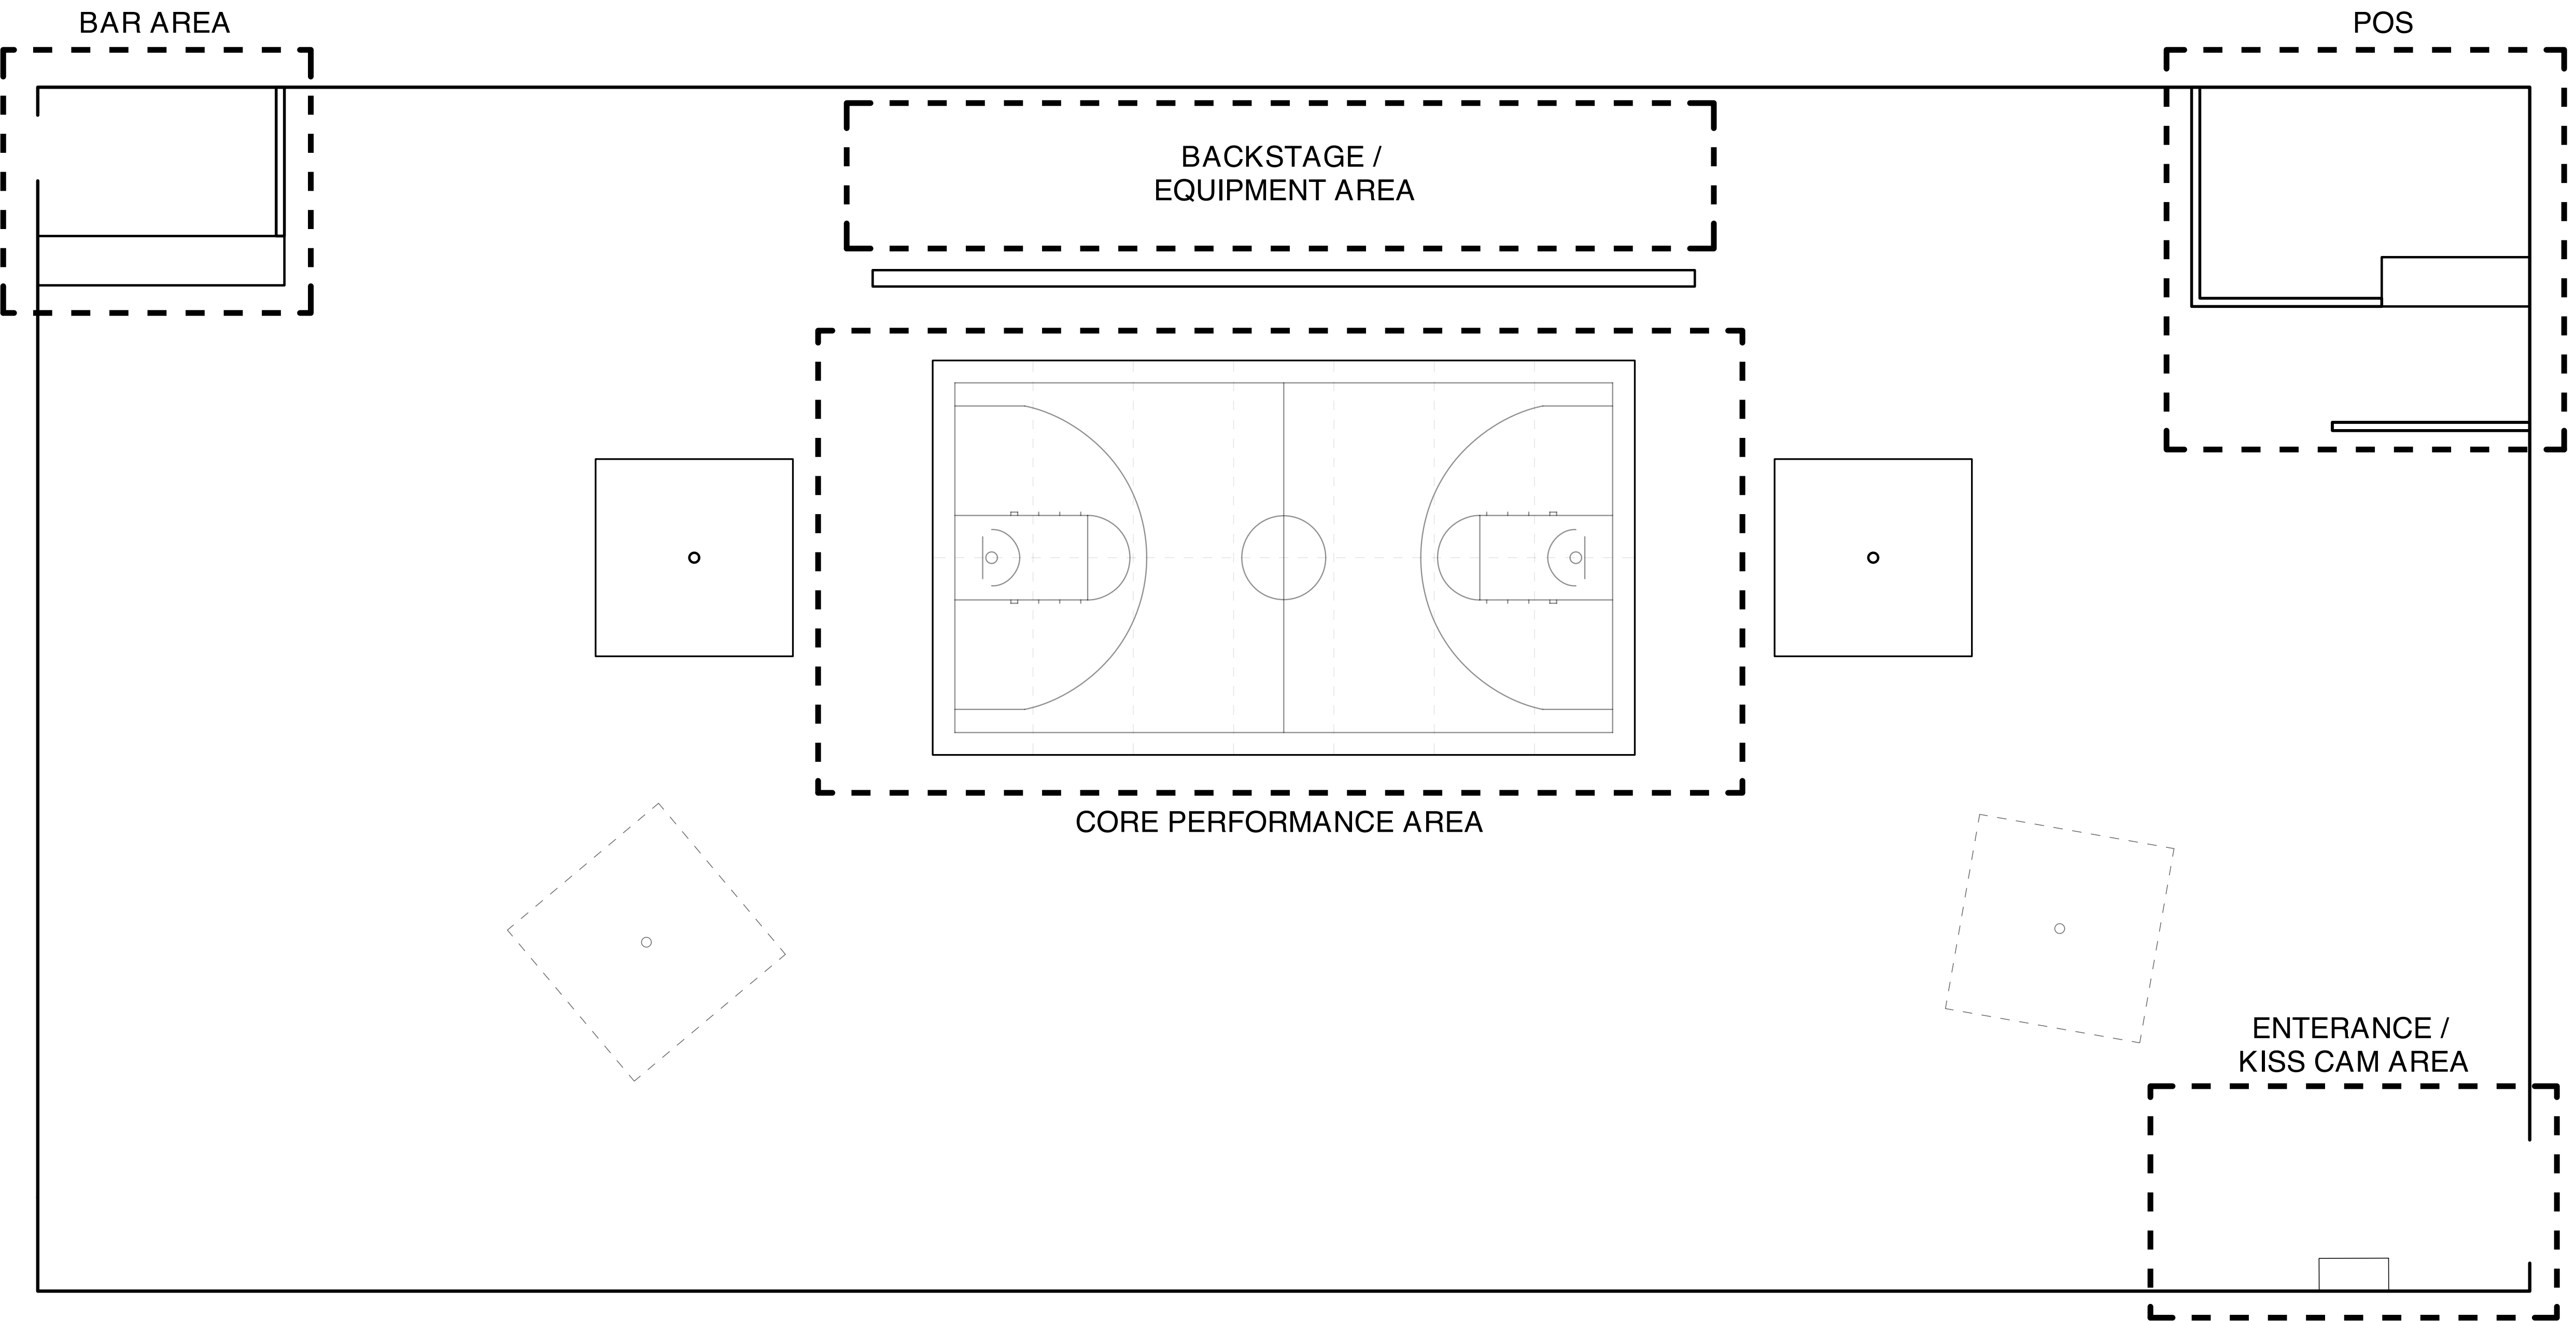

Plan: Main Functions
Bar and POS position are indicative and may adapt according to venue.

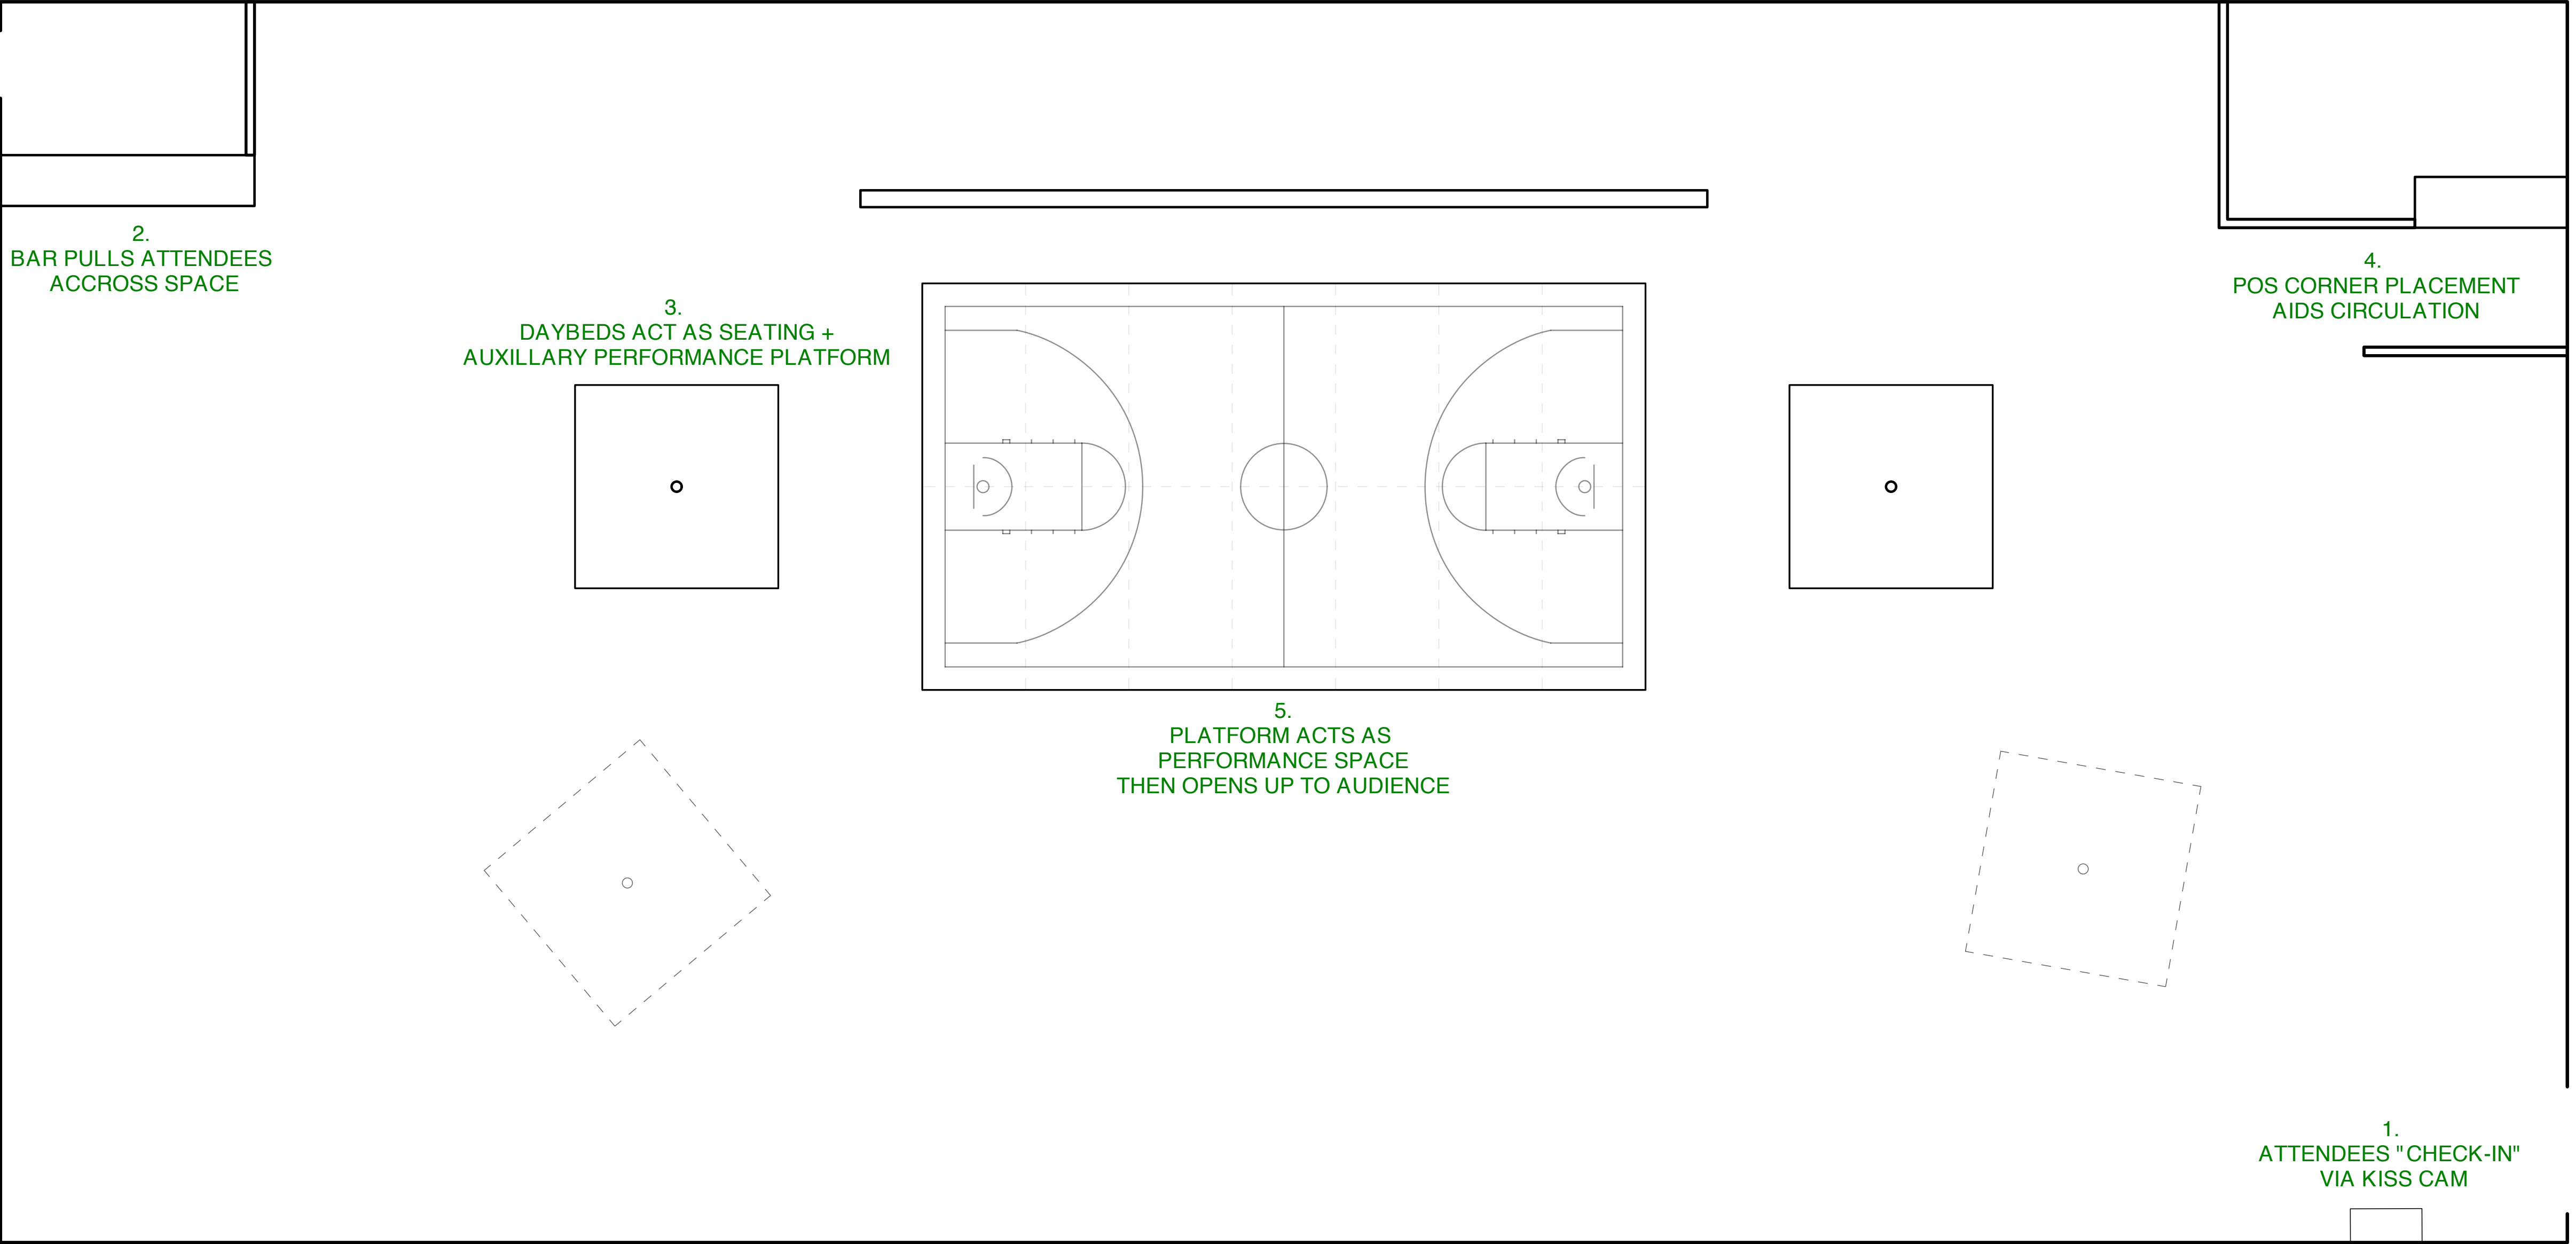

Plan: User Journey Key Points



Kiss Cam

The kiss cam is subverted through a DIY treatment. Placed at the entrance the kiss cam breaks up the user journey. The exact details of the execution are still in development and contingent on budgetary constraints. The image depicts the minimal solution.

Kiss cam images can be integrated into programming of the large LED screen.